
План участка. Отметки, уклоны, дренажные канавы

М 1:150. Север вверху, границы по каталогу координат

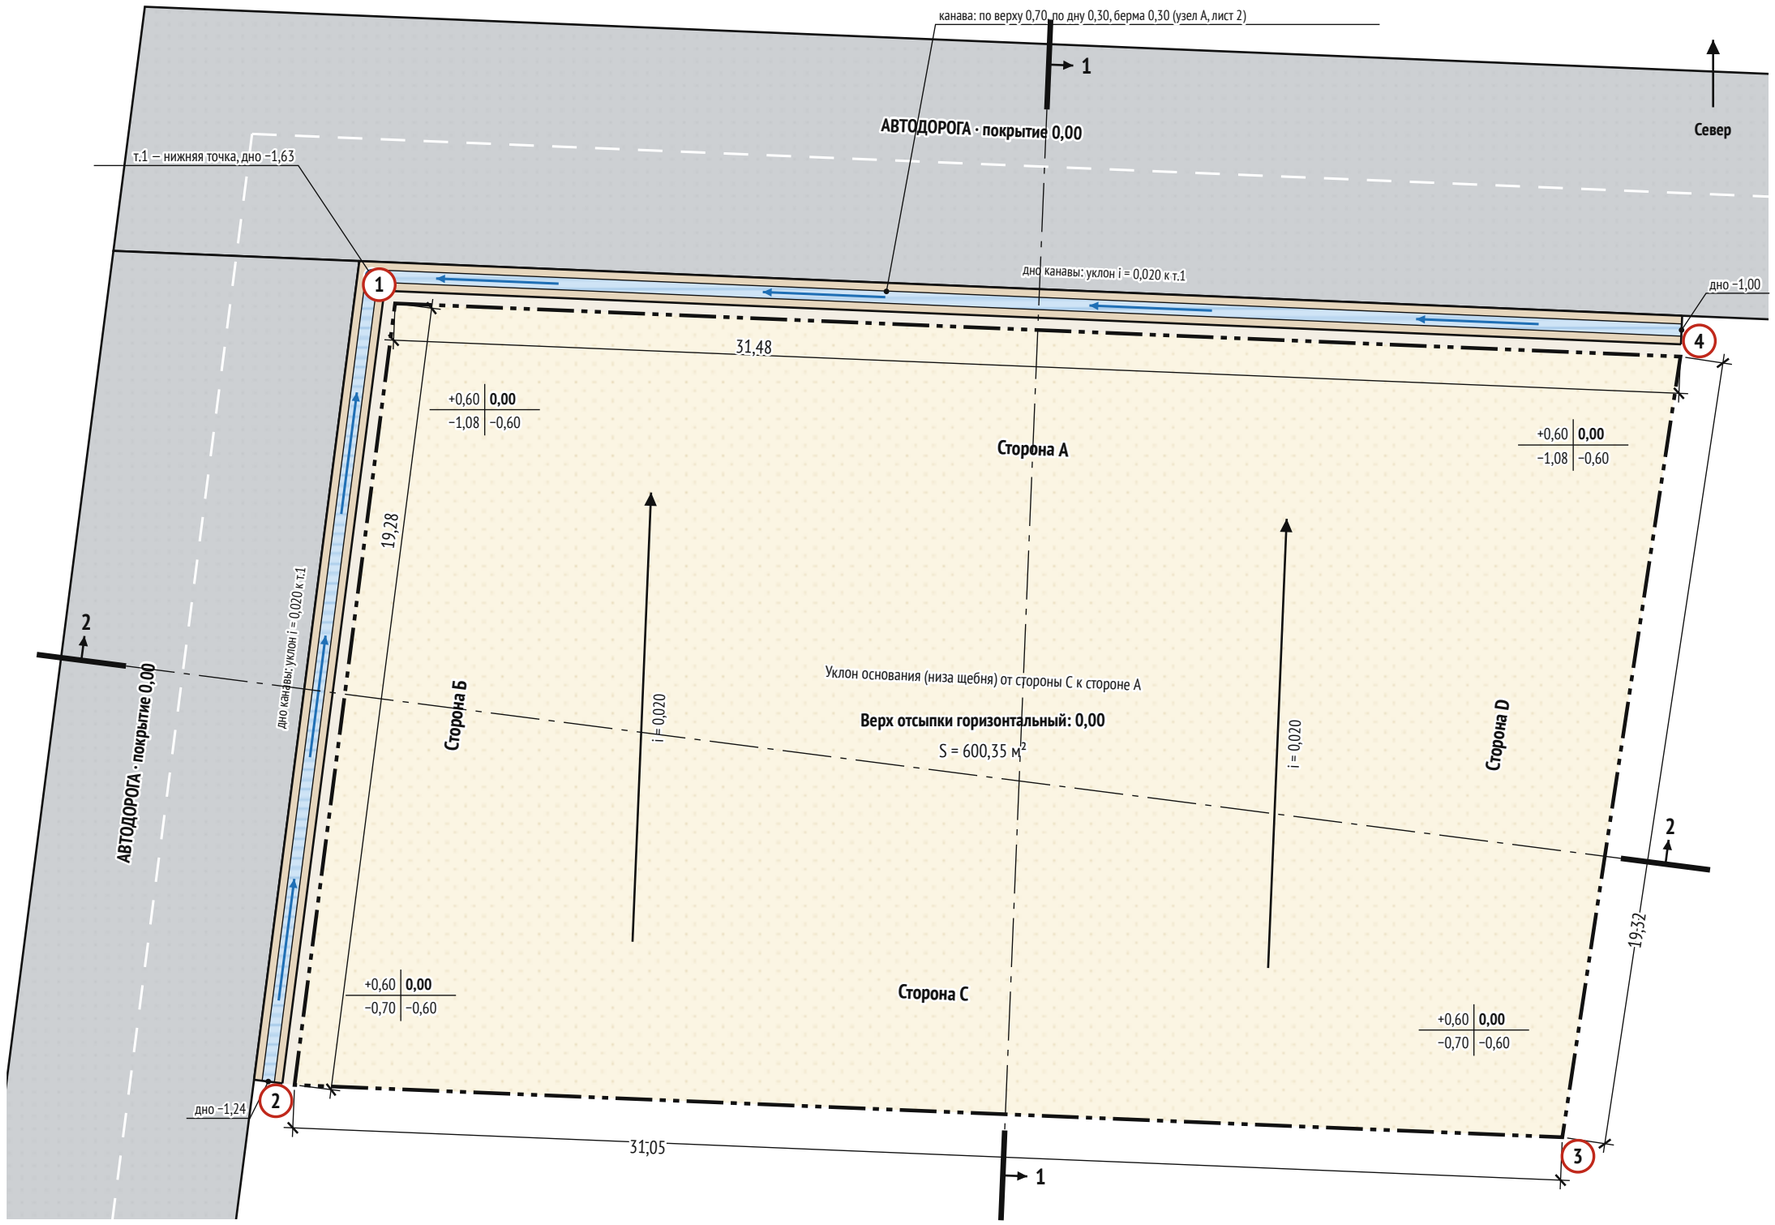

Условные обозначения

- Автодорога, покрытие 0,00
- Дренажная канава: откосы и дно
- Берма 0,30 у границы участка
- Участок, граница участка
- Сток воды по дну канавы
- Уклон основания (низа щебня)
- т.1 — самая низкая точка
- Линия разреза

Отметки в углах участка:

рабочая | **проект.**
низ щебня | существ.

рабочая = проект. − существ. (+ насыпь)

Каталог координат

№	Север	Восток	Угол	Сторона	Длина
1	523776.10	1285844.30	94°58'	Б (1–2)	19,28
2	523756.98	1285841.84	85°02'	С (2–3)	31,05
3	523755.70	1285872.86	96°14'	D (3–4)	19,32
4	523774.80	1285875.75	83°46'	А (4–1)	31,48

Ведомость отметок по углам

Угол	Проект.	Сущ.	Рабочая	Низ щебня	Срезка
1	0,00	−0,60	+0,60	−1,08	0,48
2	0,00	−0,60	+0,60	−0,70	0,10
3	0,00	−0,60	+0,60	−0,70	0,10
4	0,00	−0,60	+0,60	−1,08	0,48

Дренажная канава

Длина по оси (А + Б)	51,9 м
Ширина по верху / по дну	0,70 / 0,30 м
Отступ (берма) от границы	0,30 м
Глубина у угла 4 / у угла 2	1,00 / 1,24 м
Глубина в т.1	1,63 м
Уклон дна к т.1	0,020
Откосы	1:0,12 … 1:0,20
Ёмкость канав	35,7 м³

Примечания

1. Отметки и размеры в метрах. 0,00 — отметка покрытия автодороги. Координаты — по кадастровому плану.
2. Профиль канавы — узел А (лист 2). Разрез 1–1 — лист 2, разрез 2–2 — лист 3. Ширина автодороги условная (6,0).

Участок 600 м² у автодороги

Вертикальная планировка, отсыпка и дренаж

План участка

Отметки и размеры в метрах. 0,00 — покрытие автодороги

Стадия	Лист	Листов
Эскиз	1	3

S = 600,35 м² (по координатам углов)

М 1:150


Эскизный проект по заданию заказчика.

Не является рабочей документацией, объёмы ориентировочные.

26.10.2026


Разрез 1–1 (поперёк стороны A, посередине стороны)

М гор. 1:100, верт. 1:25

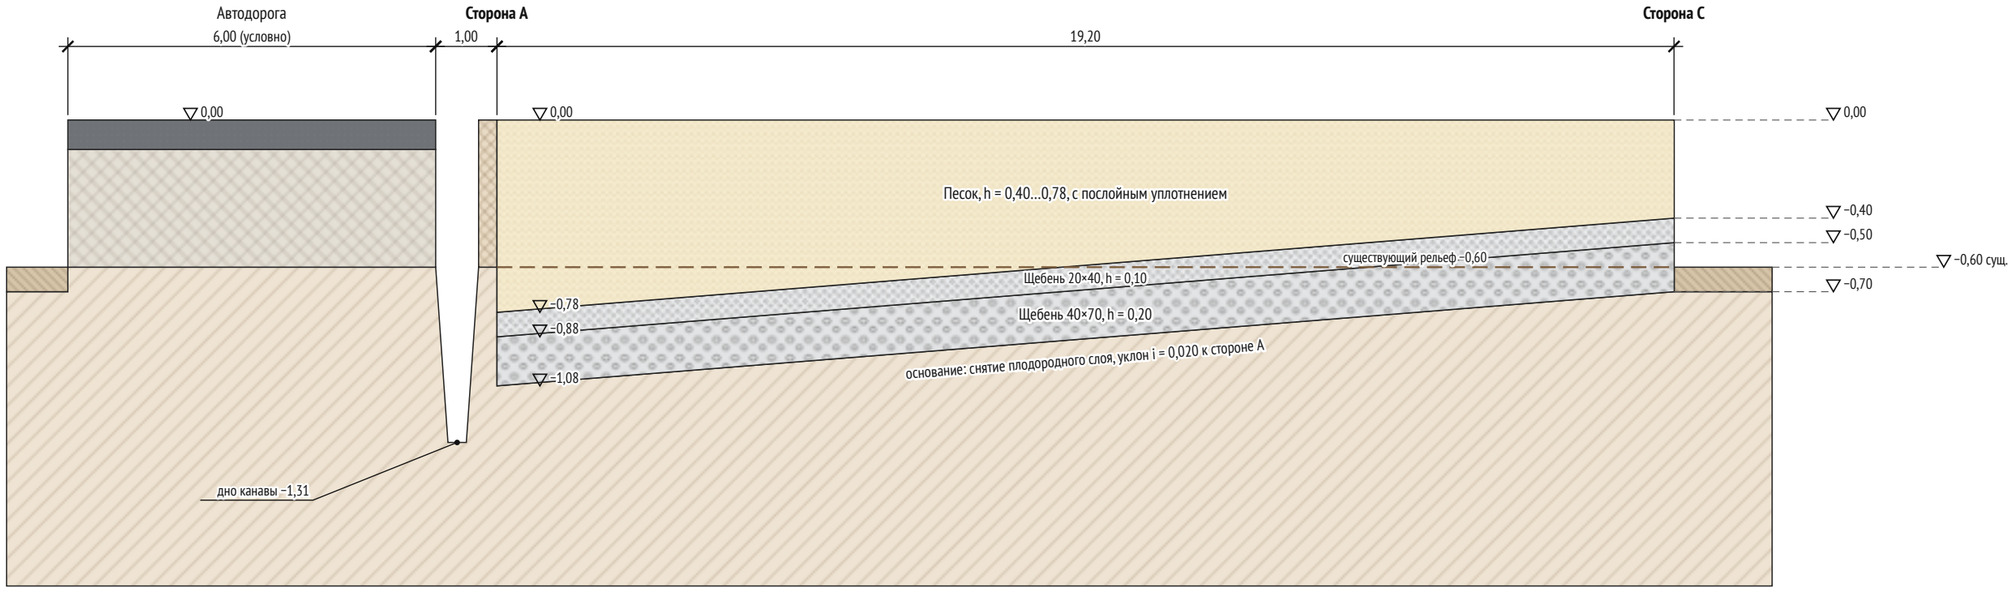

Узел A. Профиль канавы в 2 м от угла 4

М 1:25 (на остальной длине глубина больше, см. таблицу на листе 1)

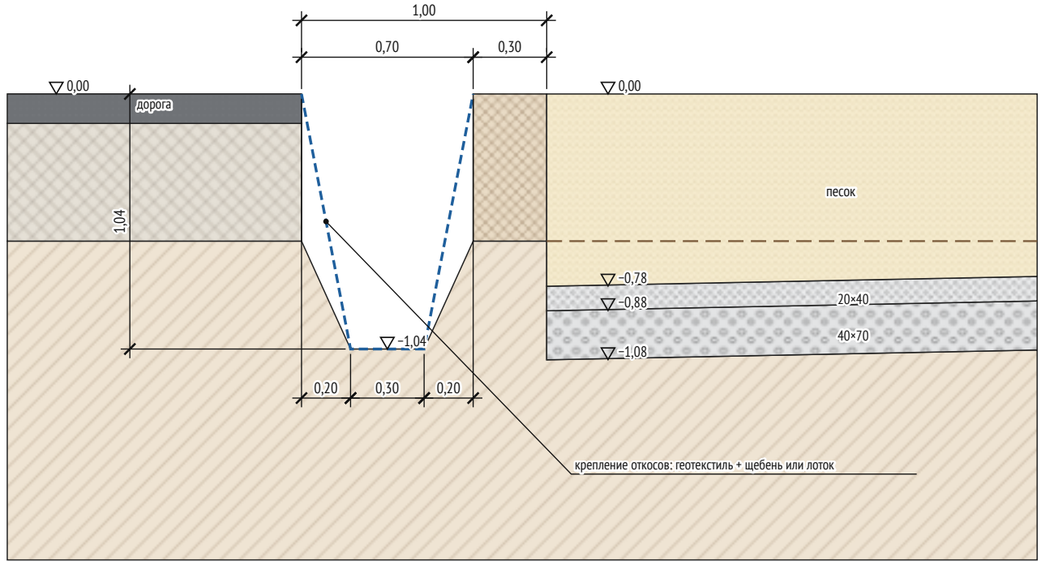


Дно канавы здесь (−1,04) на 0,04 выше низа щебня (−1,08): вода из щебня у угла 4 не уйдёт в канаву. Рекомендуется глубина в мелком конце не менее 1,20.


Откосы 1:0,19 — круче допустимого для песка (1:1,5), крепление обязательно.

Конструкция отсыпки

М 1:20

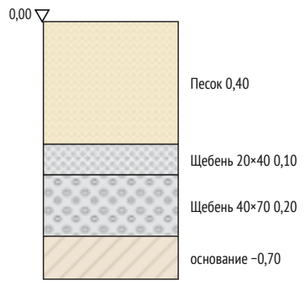

у стороны C

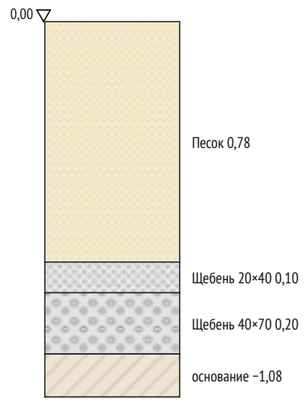

у стороны A

Порядок работ

1. Снять плодородный слой 0,10.
2. Спланировать основание с уклоном 0,020 к стороне A.
3. Вырыть канавы, уклон дна 0,020 к т.1, укрепить откосы.
4. Щебень 40×70, 0,20, уплотнить.
5. Щебень 20×40, 0,10, уплотнить.
6. Песок до 0,00, уплотнять послойно.

Участок 600 м² у автодороги

Вертикальная планировка, отсыпка и дренаж

Разрез 1–1. Узел A

Отметки и размеры в метрах. 0,00 — покрытие автодороги

Стадия	Лист	Листов
Эскиз	2	3

S = 600,35 м² (по координатам углов)

М 1:100, 1:25


Эскизный проект по заданию заказчика.

Не является рабочей документацией, объёмы ориентировочные.

26.10.2026

Разрез 2–2 (поперёк стороны Б, посередине стороны)

М гор. 1:150, верт. 1:25

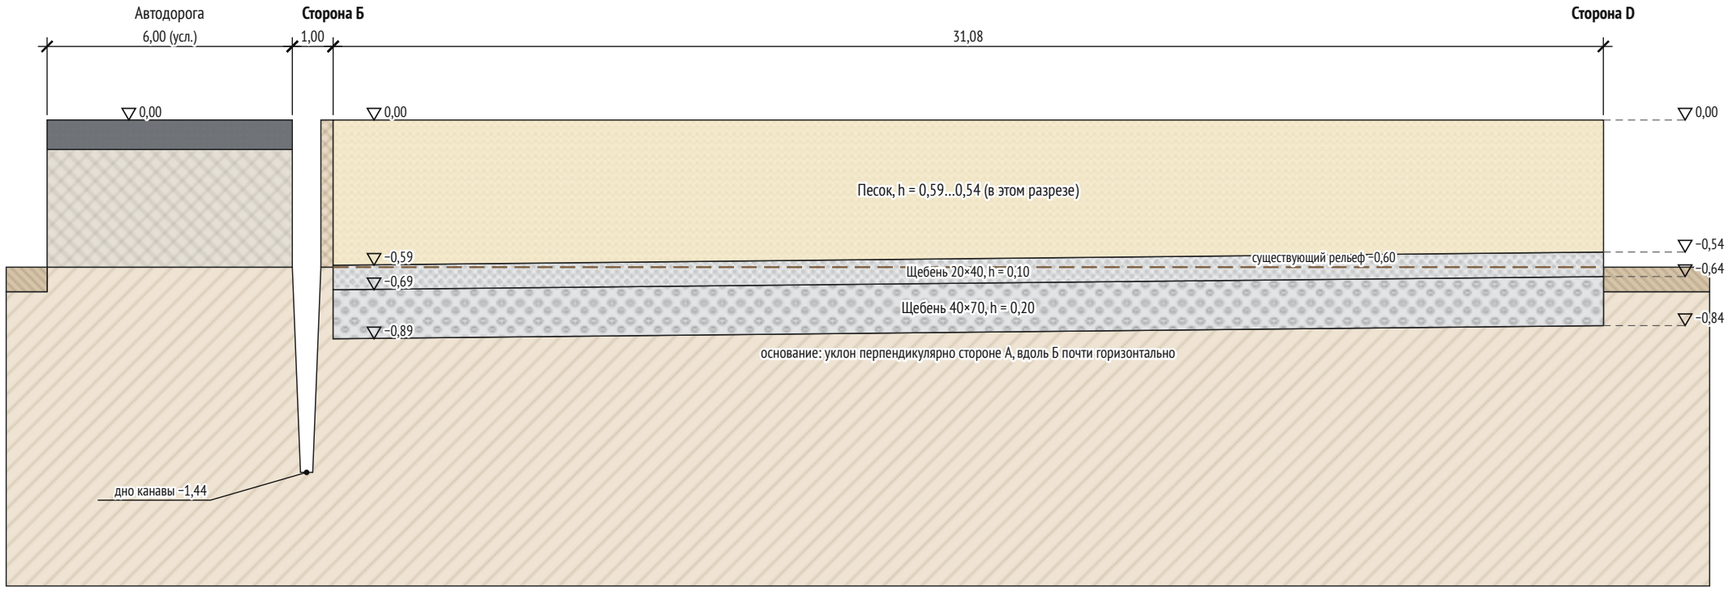

Ведомость объёмов работ и материалов

№	Наименование	Ед.	В деле	К заказу	≈ т
1	Снятие плодородного слоя 0,10	м³	60,0	–	–
2	Доп. выемка грунта под уклон основания	м³	115,6	–	–
3	Выемка грунта из канав (ниже сущ. рельефа)	м³	16,6	–	–
4	Отсыпка бермы и бортов канав	м³	12,3	–	–
5	Щебень 40×70, слой 0,20	м³	120,1	156,1	226
6	Щебень 20×40, слой 0,10	м³	60,0	78,0	109
7	Песок, слой 0,40…0,78	м³	355,7	426,9	640

К заказу = в деле × коэффициент уплотнения (щебень 1,3, песок 1,2).

Насыпная плотность: 40×70 — 1,45, 20×40 — 1,40, песок — 1,50 т/м³. Уточнить у поставщика.

Примечания

1. Отметки и размеры в метрах. Условный 0,00 — покрытие автодороги. Участок исходно ниже дороги на 0,60.
2. Границы — по каталогу координат, S = 600,35 м². Углы: 1 — 94°58', 2 — 85°02', 3 — 96°14', 4 — 83°46'.
3. Плодородный слой снимается на 0,10 у стороны С; основание с уклоном 0,020 к стороне А (у А выемка 0,48).
4. Подъём до 0,00: 0,60 + 0,10 = 0,70 = 0,20 + 0,10 + 0,40 (у стороны С). К стороне А слой песка растёт до 0,78.
5. Канавы вдоль сторон А и Б: 0,70 по верху от края дороги, берма 0,30 у границы, дно с уклоном 0,020 к т.1 (угол 1).
6. Глубина 1,00 от покрытия дороги — в мелком конце (угол 4). Рекомендуется 1,20: иначе у угла 4 дно выше низа щебня.
7. Откосы канав круче 1:1 — нужно крепление (геотекстиль + щебень, габионы или ж/б лоток).
8. Сброс воды из т.1 (колодец, труба, кювет) — по месту, в задании не определён.
9. Слои отсыпать с послойным уплотнением.
10. Ширина автодороги на чертеже условная.

Участок 600 м² у автодороги

Вертикальная планировка, отсыпка и дренаж

Разрез 2–2. Ведомость объёмов

Отметки и размеры в метрах. 0,00 — покрытие автодороги

Стадия	Лист	Листов
Эскиз	3	3

S = 600,35 м² (по координатам углов)

Эскизный проект по заданию заказчика.

Не является рабочей документацией, объёмы ориентировочные.

М 1:150, 1:25

26.10.2026